Общество с ограниченной ответственностью «Профит»

УТВЕРЖДАЮ
Генеральный директор
ООО «Профит»

_____ В.А. Палагин
21.03.2025 г.

Заключение № 905/2025
по результатам технического диагностирования внутридомового газового оборудования, установленного по адресу: Республика Татарстан, г. Казань, ул. Юлиуса Фучика, д. 105

Заказчик: ООО «АДС Приволжский»

2025г.

© Общество с ограниченной ответственностью «Профит», 2025

Содержание

		стр.
1.	Вводная часть	5
1.1.	Основания для проведения технического диагностирования	5
1.2.	Сведения о специализированной организации, проводившей техническое диагностирование	5
1.3.	Состав рабочей группы	5
2.	Перечень объектов технического диагностирования	6
3.	Данные о заказчике	7
4.	Цель технического диагностирования	7
5.	Результаты технического диагностирования	8
5.1.	Результаты анализа проектной, исполнительной и эксплуатационной документации внутридомового газового оборудования	8
5.1.1.	Перечень рассмотренной технической документации	8
5.1.2.	Технические характеристики объекта технического диагностирования	8
5.2.	Результаты оценки реальных условий эксплуатации внутридомового газового оборудования	8
5.2.1.	Внутренние газопроводы	8
5.2.2.	Состояние строительных конструкций в местах прокладки газопроводов и установки оборудования	9
5.2.3.	Наличие и состояние участков переходов газопроводов через строительные конструкции	9
5.3.	Результаты визуального и измерительного контроля внутридомового газового оборудования	10
5.4.	Результаты обследования арматуры	11
5.5.	Результаты испытания на герметичность внутридомового газового оборудования	11
5.5.1.	Наличие загазованности помещений	11
5.5.2.	Наличие утечек на внутренних и вводных газопроводах	11
5.6.	Определение срока возможного дальнейшего использования ВДГО	11
6.	Заключительная часть	12
	Приложение 1 Программа проведения технического диагностирования внутридомового газового оборудования	
	Приложение 2 Схема неразрушающего контроля	
	Приложение 3 Фото дефектного участка	
	Приложение 4 Протокол № 905/2025 по результатам ультразвуковой толщинометрии (УЗТ)	
	Приложение 5 Протокол № 905/2025по результатам ультразвукового контроля (УК) сварных соединений	
	Приложение 6 Протокол № 905/2025 по результатам контроля влажности	

	Приложение 7 Протокол № 905/2025 по результатам контроля контакта «труба-футляр»	
	Приложение 8 Протокол № 905/2025 визуального и измерительного контроля	
	Приложение 9 Протокол № 905/2025 по результатам контроля на герметичность	
	Приложение 10 Акт по результатам пневматического испытания	
	Приложение 11 Расчёт срока возможного дальнейшего использования ВДГО	
	Приложение 12 Согласованные мероприятия по устранению неисправностей, выявленных при проведении технического диагностирования	
	Приложение 13 Копии удостоверений специалистов неразрушающего контроля и лиц, ответственных за проведение технического диагностирования	
	Приложение 14 Листы учета проведения технического диагностирования (первичный выезд для проведения работ по ТД ВДГО)	
	Приложение 15 Акт отсутствия доступа в жилые помещения (первичный выезд для проведения работ по ТД ВДГО)	
	Приложение 16 Листы учета проведения технического диагностирования (повторный выезд для проведения работ по ТД ВДГО)	
	Приложение 17 Акт отсутствия доступа в жилые помещения (повторный выезд для проведения работ по ТД ВДГО)	
	Приложение 18 Перечень нормативной, технической и методической документации, используемой при проведении технического диагностирования	

1. Вводная часть

1.1 Основания для проведения технического диагностирования:

Техническое диагностирование проведено в целях исполнения Постановления Правительства Российской Федерации от 14 мая 2013 года № 410 (с изменениями и дополнениями) «О мерах по обеспечению безопасности при использовании и содержании внутридомового и внутриквартирного газового оборудования», в связи с истечением срока эксплуатации, установленного в отношении газопровода.

1.2 Сведения о специализированной организации, проводившей техническое диагностирование

Полное наименование	Общество с ограниченной ответственностью «Профит»
Краткое наименование	ООО «Профит»
Юридический адрес	420133, Республика Татарстан, г. Казань, ул. Аделя Кутуя, д. 110Д
Телефон / факс	+7 (917) 879-86-96
Генеральный директор	Палагин Виталий Александрович

1.3 Состав рабочей группы

Для выполнения работ по техническому диагностированию объекта приказом № 8Б от 09.01.2024 г директора ООО «Профит» назначена рабочая группа:

Ф.И.О.	№ удостоверения, кем и когда выдано
Козлов Александр Александрович	Квалификационное удостоверение специалиста 2 уровня УК, ВИК № 0039-11-28361 от 07.07.2023 г. Независимый орган аттестации персонала в области НК ООО «Лидер НК» Слесарь по эксплуатации и ремонту газового оборудования 5 разряда, удостоверение № 1/22-10-20-00040 от 20.10.2022 г., АНО ДПО УЧЕБНЫЙ ЦЕНТР «ПРОМСТОЙГАЗ», протокол № ПО 22-10-20-00022 от 20.10.2022 г.
Валиуллин Эдуард Фардинантович	Слесарь по эксплуатации и ремонту газового оборудования, удостоверение № 826 от 06.02.2025 г., АНО ДПО УТЦ «Профессионал», г. Владимир

Копии квалификационных удостоверений специалистов представлены в Приложении 13.

2 Перечень объектов технического диагностирования

Действие настоящего заключения распространяется на внутридомовое газовое оборудование, установленное по адресу: Республика Татарстан, г. Казань, ул. Юлиуса Фучика, д. 105

№	Наименование объекта	Количество (протяженность) п.м.	Разрешенное давление, МПа
1	Внутренний газопровод	381,85	0,003

3 Данные о заказчике:

Полное наименование организации	Общество с ограниченной ответственностью «АДС Приволжский»
Сокращенное наименование организации	ООО «АДС Приволжский»
Юридический адрес	420141, Республика Татарстан, г. Казань, ул. Комиссара Габишева, д. 39, помещ. 2
Телефон	+7 843 202-30-29
Директор	А.М. Васильев

4 Цель технического диагностирования

4.1 Определение фактического технического состояния внутридомового газового оборудования и его составных частей.

4.2 Поиск и определение неисправностей внутридомового газового оборудования.

4.3 Определение возможности дальнейшего использования внутридомового газового оборудования.

5. Результаты технического диагностирования

5.1. Результаты анализа проектной, исполнительной и эксплуатационной документации внутридомового газового оборудования:

5.1.1. Перечень рассмотренной технической документации:

№ п/п	Наименование документа	Примечание
1.	Проект	Не предоставлен
2.	Эксплуатационный паспорт	Не предоставлен
3.	Договор на техническое обслуживание	Договор «О техническом обслуживании и ремонте внутридомового/внутриквартирного газового оборудования» с ООО «Газпром трансгаз Казань»

5.1.2 Технические характеристики объекта технического диагностирования:

№ п/п	Наименование объекта	Дата ввода в эксплуатацию	Протяженность(м)	Количество сварных стыков (шт.)	Наличие переходов через строительные конструкции	Дата проведения последнего обслуживания, ремонта, диагностирования	Выявленные неисправности в процессе эксплуатации
1	Внутренний газопровод	Нет данных					

5.1.3 Схема неразрушающего контроля внутридомового газового оборудования представлена в Приложении 2.

5.2. Результаты оценки реальных условий эксплуатации внутридомового газового оборудования

5.2.1. Внутренние газопроводы

Наименование	Внутренний газопровод
Дата ввода в эксплуатацию	Нет данных
Материал	Сталь
Условный проход газопровода Ду, мм	32, 25, 20, 15
Минимальная толщина стенки, S_{min}	2,4
Максимальная толщина стенки, S_{max}	3,2
Способ соединения участков газопровода	Сварное, резьбовое
Способ прокладки газопровода	Надземный
Состояние защитного покрытия	Удовлетворительно
Наличие участков с агрессивными средами	Не обнаружено

5.2.2 Состояние строительных конструкций в местах прокладки газопроводов и установки оборудования:

Наименование	Внутренний газопровод
Наименование строительной конструкции	Стена, перекрытия
Материал строительной конструкции	Ж/б панель, ж/б плита
Наличие разрушений и трещин	Не обнаружено
Наличие влажности, агрессивного воздействия	Не обнаружено
Наличие контактов газопровода со строительной конструкцией	Не обнаружено, кроме см. часть 6, п.1.3, 1.5, 1.9
Выявленные неисправности и несоответствия	Контакт газопровода со стр. конструкцией

5.2.3 Наличие и состояние участков переходов газопроводов через строительные конструкции:

Наименование	Внутренний газопровод
Материал газопровода	Сталь
Условный проход газопровода Ду, мм	32, 25, 20
Наименование строительной конструкции	Стена, перекрытия
Материал строительной конструкции	Ж/б панель, ж/б плита
Наличие футляра	В наличии
Наличие коррозионных повреждений	Не обнаружено
Наибольшая влажность конструкции, %	1,3
Состояние заделки пространства между газопроводом и футляром	Удовлетворительно, кроме см. часть 6, п.1.1, 1.7
Количество контактов труба-футляр	-
Выявленные неисправности и несоответствия	Дефект заделки

5.3. Результаты визуального и измерительного контроля внутридомового газового оборудования Приложение 8.

Вывод: состояние элементов газопроводов соответствует требованиям нормативно-технической документации не в полной мере.

5.4. Результаты обследования арматуры (за исключением арматуры, расположенной в помещениях, указанных в Приложении 17)

Место установки	Условный проход Ду, мм	Тип Запорной арматуры	Параметры, подлежащие контролю				Заключение
			Состояние наружной поверхности	Наружная герметичность	Внутренняя герметичность	Проверка работоспособности	
Подъезд № 2	32	Пробковый, шаровый	Удовл.	Герметичны	Герметичны	Исправны	Допускаются к дальнейшей эксплуатации
Квартиры № 1-70	15	Пробковый, шаровый	Удовл.	Герметичны	Герметичны	Исправны	Допускаются к дальнейшей эксплуатации
Подъезд № 1-2, кран на стояк № 1-8, кран на вводе № 1	32, 25	Пробковый, шаровый	Неудовл.	Герметичны	Нет данных	Нет данных	Допускаются к дальнейшей эксплуатации после проведения обслуживания

Вывод: Подъезд № 1-2, кран на стояк № 1-8, кран на вводе № 1 не обслужен. Остальная арматура исправна и допускается к дальнейшей эксплуатации.

5.5. Результаты испытания на герметичность внутридомового газового оборудования

5.5.1. Наличие загазованности помещений – не обнаружено.

5.5.2. Наличие утечек на внутренних и вводных газопроводах и газовом оборудовании

№ п/п	Местоположение утечки	Ф.И.О. собственника
1	-	-

Проверка газопровода на герметичность не проводилась в связи с отсутствием технической возможности её проведения по причине отсутствия доступа во все жилые помещения при первичном обходе и по причине необслуженной запорной арматуры (Подъезд № 1-2, кран на стояк № 1-8, кран на вводе № 1).

5.6. Определение срока возможного дальнейшего использования ВДГО:

На основании проведённого расчёта (см. Приложение 11) срок возможного дальнейшего использования ВДГО составляет 3 года. Указанный срок не является предельным сроком эксплуатации газопровода.

6. Заключительная часть

6.1 Неисправности, выявленные в результате технического диагностирования внутридомового газового оборудования:

№ п/п	Место расположения	Наименование неисправности
1.	Внутренний газопровод	
1.1	Подъезд №1, условный проход Ду32	Нарушение технологии заделки футляра (СП 42-101-2003 (п.6.7)).
1.2	Подъезд №1, условный проход Ду32, 25, смотри схему контроля, фото 3, 4, 7, 8, 10.	Техническое обслуживание запорной арматуры не проведено (Постановление Правительства РФ от 14 мая 2013 г. N 410).
1.3	Подъезд №1, условный проход Ду25, смотри схему контроля, фото 4, 7.	Касание газопровода со строительной конструкцией (СП 42-101-2003 (п.6.7)).
1.4	Подъезд №1, условный проход Ду32, 25, смотри схему контроля, фото 1-5, 7.	Провода и кабели вблизи газопровода (СП 42-101-2003 (п.6.6); ПУЭ (п.2.1.56, п.2.1.57)).
1.5	Подъезд №1, условный проход Ду25, смотри схему контроля, фото 7.	Касание газопровода со строительной конструкцией СП 42-101-2003 (п.10.216).
1.6	Подъезд №1, условный проход Ду32, 25, смотри схему контроля, фото 2, 5.	Газопровод вблизи строительной конструкции СП 42-101-2003 (п.10.216).
1.7	Подъезд №2, условный проход Ду32, смотри схему контроля, фото 12, 15.	Нарушение технологии заделки футляра (СП 42-101-2003 (п.6.7)).
1.8	Подъезд №2, условный проход Ду25, смотри схему контроля, фото 11, 13, 14, 17.	Техническое обслуживание запорной арматуры не проведено (Постановление Правительства РФ от 14 мая 2013 г. N 410).
1.9	Подъезд №2, условный проход Ду32, 25, смотри схему контроля, фото 13, 14, 17, 18, 19.	Касание газопровода со строительной конструкцией (СП 42-101-2003 (п.6.7)).
1.10	Подъезд №2, условный проход Ду32, 25, смотри схему контроля, фото 11, 14, 16, 19, 20.	Провода и кабели вблизи газопровода (СП 42-101-2003 (п.6.6); ПУЭ (п.2.1.56, п.2.1.57)).
1.11	Подъезд №2, условный проход Ду32, 25, смотри схему контроля, фото 16, 17, 20.	Газопровод вблизи строительной конструкции СП 42-101-2003 (п.10.216).

6.2 Дальнейшее использование обследованного внутридомового газового оборудования допустимо при условии:

- устранения выявленных неисправностей и причин их возникновения в объеме, соответствующем дефектной ведомости (Приложение 12);

- отсутствия неправомерно подключенного газоиспользующего оборудования;

Использование внутридомового газового оборудования с неустраненными неисправностями, выявленными в ходе технического диагностирования не допускается (постановлением Правительства Российской Федерации от 14 мая 2013 года N 410 (с изменениями и дополнениями).

6.3 Рекомендации по обеспечению безопасного использования и улучшению условий эксплуатации внутридомового газового оборудования:

- устранить выявленные неисправности в полном объеме;

- соблюдать сроки ежегодного технического обслуживания внутридомового и (или) внутриквартирного газового оборудования;

- провести контроль параметров запорной арматуры во всех жилых помещениях (квартирах) указанных в Приложении 17;

- следующее техническое диагностирование внутридомового газового оборудования провести не позднее марта 2028 года;

- обеспечить выполнение требований, установленных Правилами пользования газом в части обеспечения безопасности при использовании и содержании внутридомового и внутриквартирного газового оборудования при предоставлении коммунальной услуги по газоснабжению, утвержденными постановлением Правительства Российской Федерации от 14 мая 2013 года N 410 (с изменениями и дополнениями).

Специалист II-го уровня квалификации Квалификационное удостоверение № 0039-11-28361 (УК, ВИК) от 07.07.2023 г.	_____	А.А. Козлов
	Подпись	Ф.И.О.
С результатами ознакомлен: Директор ООО «АДС Приволжский»	_____	А.М. Васильев
	Подпись	Ф.И.О.

Приложение 1

СОГЛАСОВАНО
Директор
ООО «АДС Приволжский»

_____А.М. Васильев

УТВЕРЖДАЮ
Генеральный директор
ООО «Профит»

_____В.А. Палагин

Программа проведения технического диагностирования внутридомового газового оборудования, установленного по адресу: Республика Татарстан, г. Казань, ул. Юлиуса Фучика, д. 105

№	Перечень видов работ	Параметры
1.	Анализ предоставленной заказчиком технической документации	Наличие неисправностей и их влияние на техническое состояние оборудования. Изменение параметров технического состояния оборудования в сравнении с параметрами технического состояния при приемке в эксплуатацию или по результатам предыдущего технического диагностирования.
2.	Определение условий эксплуатации ВДГО	Соответствие либо несоответствие условий эксплуатации оборудования проектной (при наличии) и действующей нормативной документации. Условия расположения внутридомового газового оборудования. Наличие смежных коммуникаций. Наличие переходов через строительные конструкции. Наличие агрессивных сред, в том числе: - определение наличия следов протечек, степени влажности и периодичности увлажнения строительных конструкций в местах их пересечения с газопроводами, определение месторасположения газопровода относительно потенциальных источников увлажнения; - определение поверхностной и объемной влажности строительной конструкции; - определение наличия электрического контакта «труба-футляр»; - определение количества «хлорида-ионов» в материале, из которого выполнена строительная конструкция - определение значения поверхностного потенциала газопровода или его футляра в местах контакта со строительной конструкцией

Продолжение Приложения 1

3.	**Определение технического состояния внутренних газопроводов**	
3.1.	Проверка загазованности помещений	Загазованность помещений переносными газоиндикаторами
3.2.	Проверка герметичности газопровода	Наличие утечек газа на газопроводах и (или) оборудовании высокочувствительными газоиндикаторами или пенообразующим раствором.
3.3	Проверка герметичности газопровода	Проведение пневматических испытаний газопровода (опрессовки рабочим давлением). Пневматические испытания газопровода не проводятся в следующих случаях: на газопроводе имеется неисправная или неработоспособная запорная арматура; доступ специалистов обеспечен не во все квартиры жилого многоквартирного дома, имеющего газовые колонки, либо котлы; на газопроводе имеется не устраненные утечки газа; отсутствует техническая возможность для проведения пневматических испытаний
3.3.	Проверка состояния защитного покрытия и поверхности трубы газопровода	С применением метода визуального и измерительного контроля. Повреждения защитного покрытия, наличие коррозионных повреждений, толщина менее допустимой (2 мм), овальность, вмятины, задиры
3.4.	Проверка состояния сварных стыков	С применением метода визуального и измерительного контроля, ультразвукового контроля. Трещины, прожоги, кратеры, поры, подрезы. Наличие развивающихся дефектов.
3.5.	Проверка состояния переходов газопровода через строительные конструкции	С применением методов визуального и измерительного контроля, ультразвукового контроля. Отсутствие футляра (гильзы), наличие контакта «труба-футляр (гильза)», нарушение конструкции переходов, наличие коррозионных повреждений, наличие сварных стыков.
4.	**Определение параметров технического состояния надземных (наружных фасадных) газопроводов**	
4.1.	Проверка герметичности газопровода	Наличие утечек газа на газопроводах и (или) оборудовании высокочувствительными газоиндикаторами или пенообразующим раствором.
4.2.	Проверка состояния защитного покрытия и поверхности трубы газопровода	С применением метода визуального и измерительного контроля
4.3.	Проверка состояния поверхности и геометрические размеры трубы	С применением метода визуального и измерительного контроля

Продолжение Приложения 1

4.4.	Проверка состояния сварных стыков	С применением метода визуального и измерительного контроля, ультразвукового контроля. Если состояния сварных стыков по результатам ВИК оцениваются как неудовлетворительные и при этом имеется техническая возможность проведения контроля. В случае отсутствия сварных стыков, находящихся в неудовлетворительном состоянии по результатам ВИК, ультразвуковому контролю подвергается один любой стык, находящийся в наиболее неблагоприятных условиях.
4.5.	Проверка состояние крепления газопровода	Положение трубы и опор газопровода методом визуального и измерительного контроля
4.6.	Проверка состояния электроизолирующих соединений	С применением измерительного контроля мультиметр цифровой
5.	Определение параметров технического состояния арматуры (запорная, предохранительная)	Проверка с применением методов визуального и измерительного контроля: -состояния наружной поверхности; -герметичности (наружная и внутренняя) запорной арматуры поиском утечек газа высокочувствительными газоиндикаторами или пенообразующим раствором; -работоспособности на функционирование. -наличие воды, грязи (препятствующих работе газового оборудования), ржавчины, перекосов, раковин, трещин, механические и коррозионные повреждения, нарушения защитного покрытия.
6.	Фотодокументирование дефектных участков	Выполняется при наличии дефектов
7.	**Анализ результатов технического диагностирования и определение возможности дальнейшего использования**	
7.1	Анализ результатов технического диагностирования ВДГО.	Учет неисправностей и их влияние на техническое состояние оборудования. Учет изменения параметров технического состояния оборудования в сравнении с параметрами технического состояния при приемке в эксплуатацию или по результатам предыдущего технического диагностирования. Учет влияния условий эксплуатации на возникновение неисправностей газового оборудования.
7.2	Разработка мероприятий по обеспечению безопасной эксплуатации внутридомового газового оборудования.	Разработка мероприятий по обеспечению надежной и безопасной эксплуатации. Разработка мероприятий по ремонту газопроводов и газового оборудования.
7.3	Расчет	Определение срока возможного дальнейшего использования ВДГО.

Продолжение Приложения 1


7.4	Составление сводной ведомости дефектов внутридомового газового оборудования	Составляется при наличии обнаруженных дефектов.
8.	Составление заключения по результатам технического диагностирования внутридомового газового оборудования каждого многоквартирного дома	Отдельно по каждому многоквартирному жилому дому
9.	Изготовление эксплуатационного паспорта	Выдача Эксплуатационных паспортов газопровода производится в соответствии с требованиями ГОСТ Р 54983-2012 «Системы газораспределительные. Сети газораспределения природного газа. Общие требования к эксплуатации. Эксплуатационная документация».

Специалист II-го уровня квалификации
Квалификационное удостоверение
№ 0039-11-28361 (УК, ВИК) от 07.07.2023 г. _____ А.А. Козлов

Подпись Ф.И.О.

Приложение 2

Схема
неразрушающего контроля
внутридомового газового оборудования
по адресу : Республика Татарстан, г. Казань, ул. Юлиуса Фучика, д. 105 (подъезд 1)

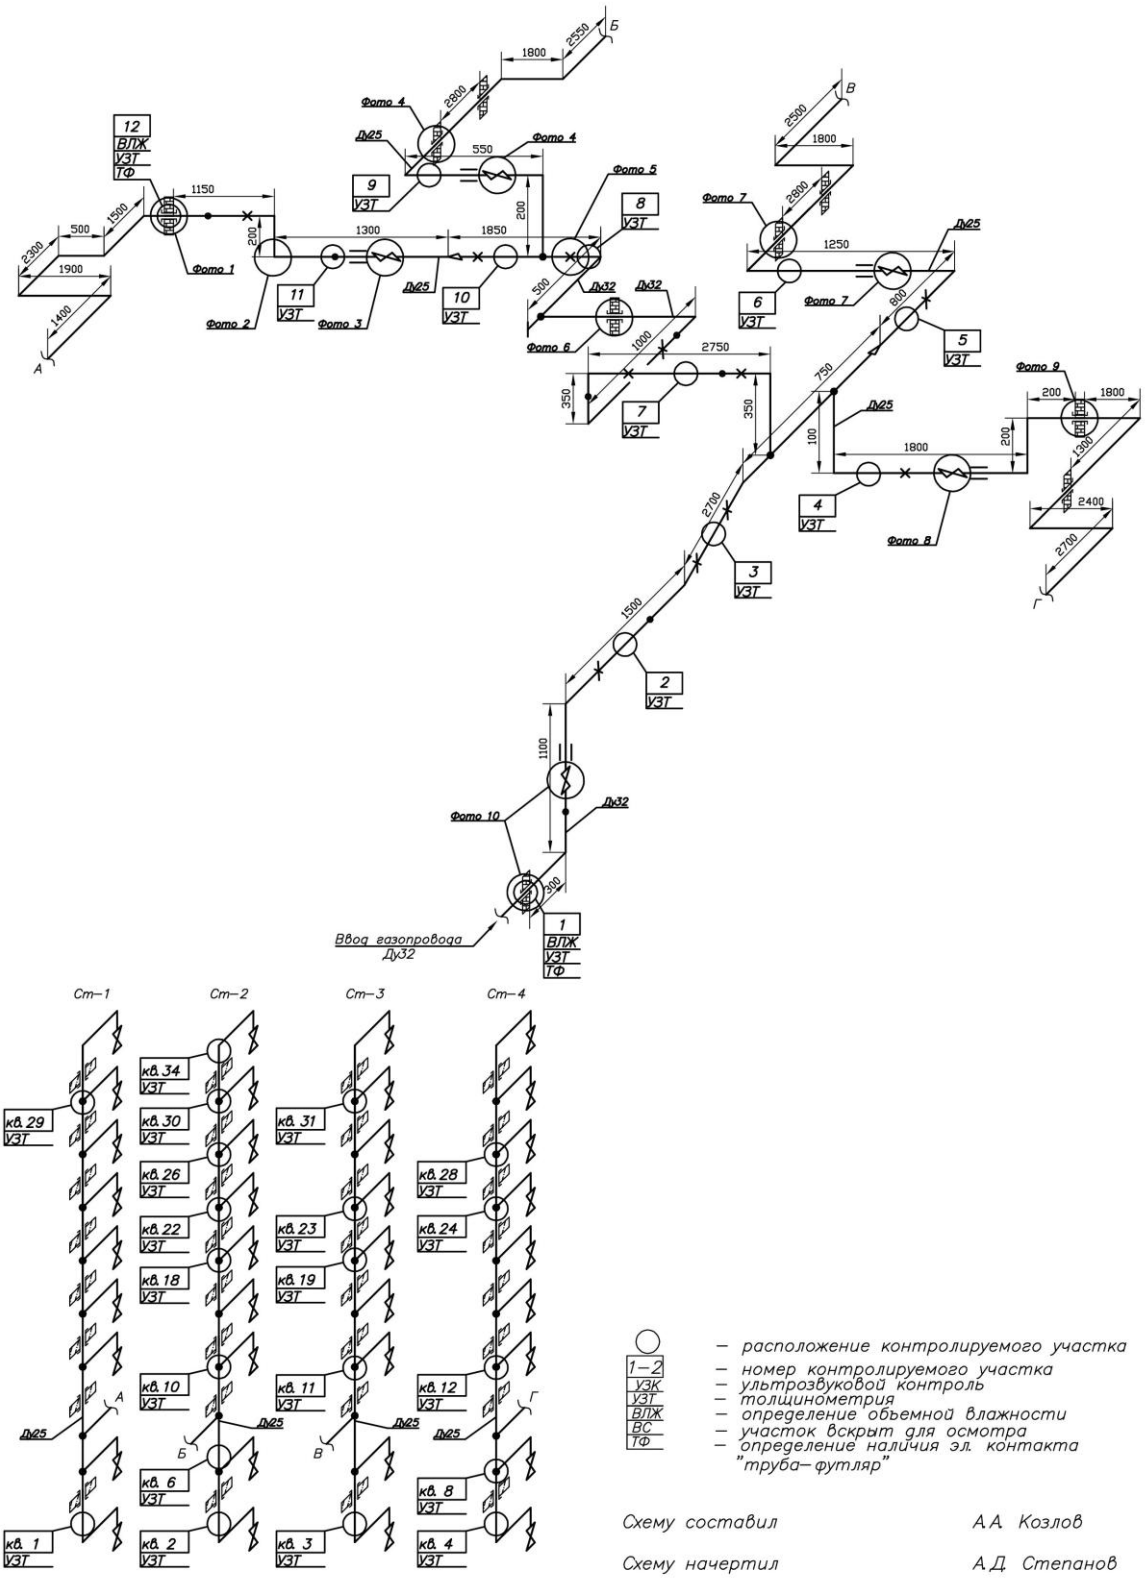



Схему составил А.А. Козлов

Схему начертил А.Д. Степанов

Продолжение Приложения 2

Схема
неразрушающего контроля
внутридомового газового оборудования
по адресу : Республика Татарстан, г. Казань, ул. Юлиуса Фучика, д. 105 (подъезд 2)

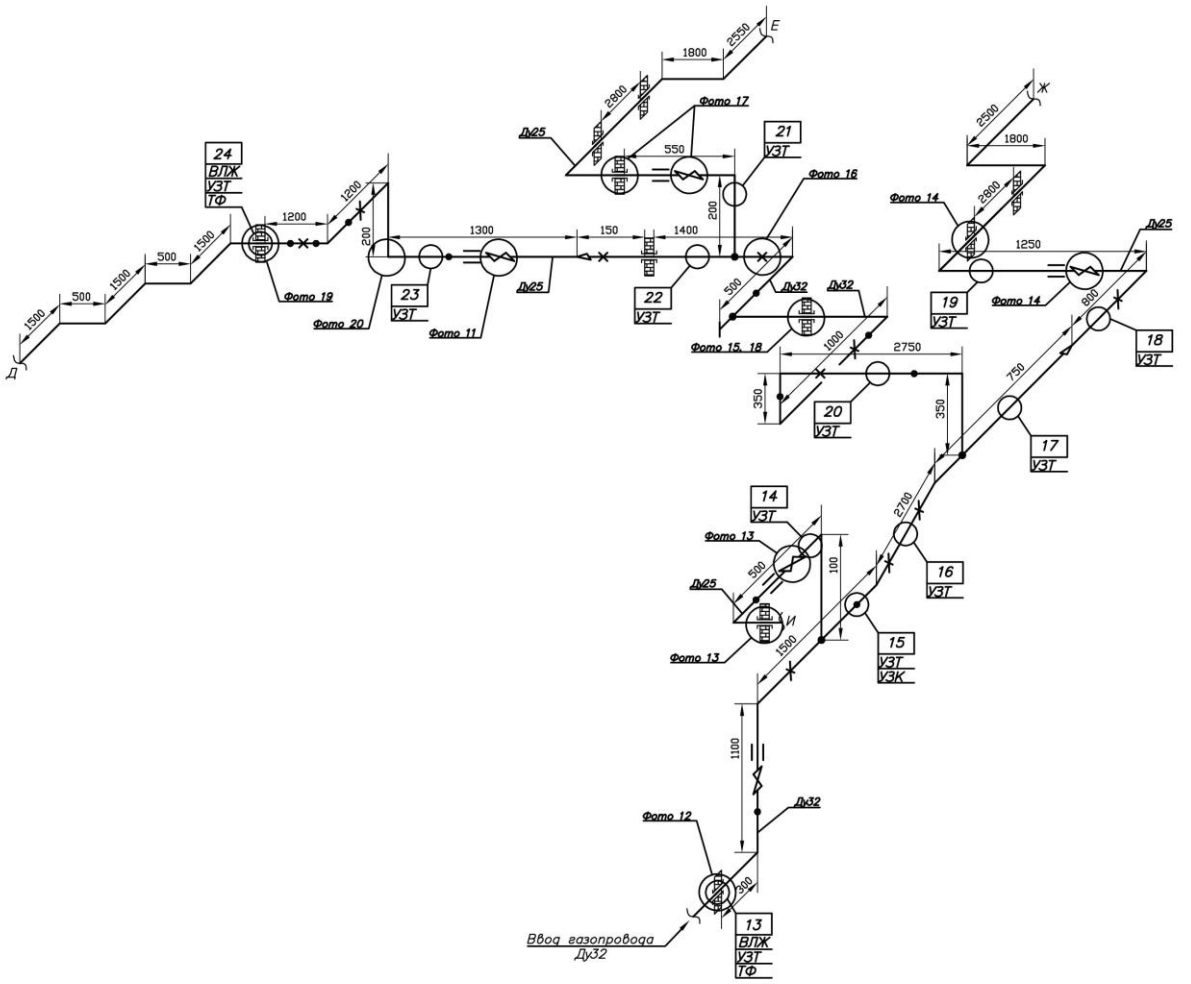

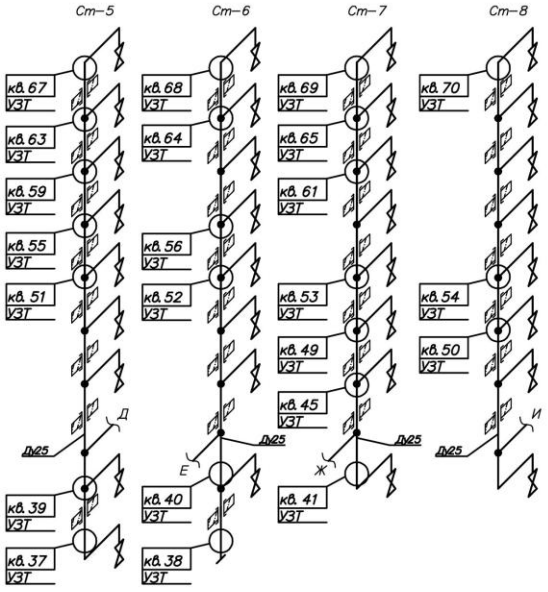

○	– расположение контролируемого участка
1–2	– номер контролируемого участка
УЗК	– ультрозвуковой контроль
УЗТ	– толщинометрия
ВЛЖ	– определение объемной влажности
ВС	– участок вскрыт для осмотра
ТФ	– определение наличия эл. контакта "труба–футляр"

Схему составил *А.А. Козлов*

Схему начертил *А.Д. Степанов*

Приложение 3

Фото дефектного участка

Фото 1



Фото 2




Продолжение Приложения 3

Фото дефектного участка

Фото 3



Фото 4

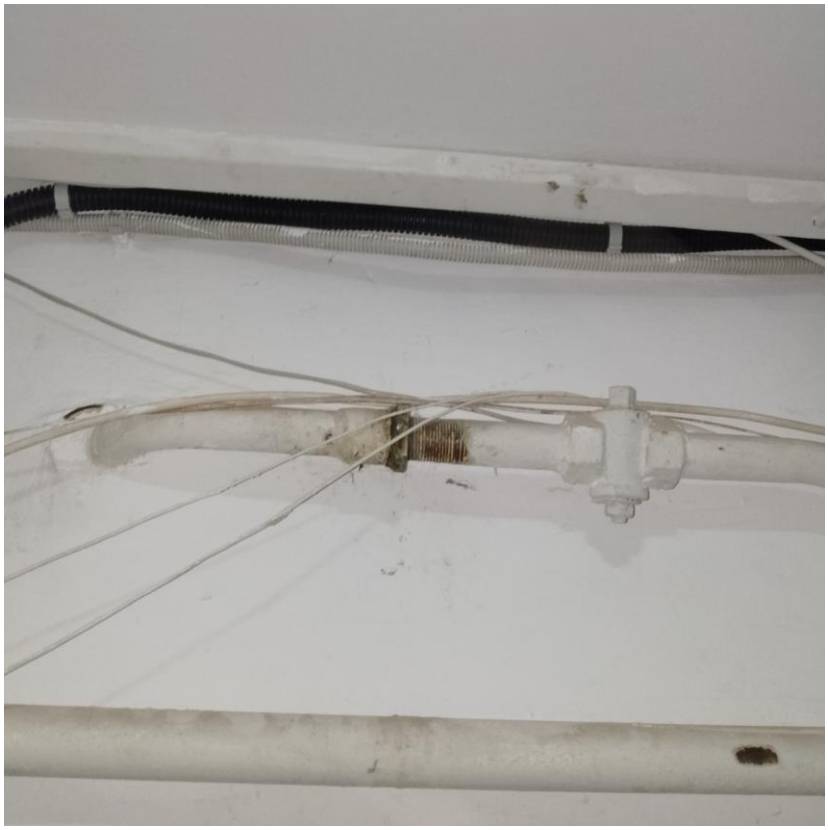

Продолжение Приложения 3

Фото дефектного участка

Фото 5

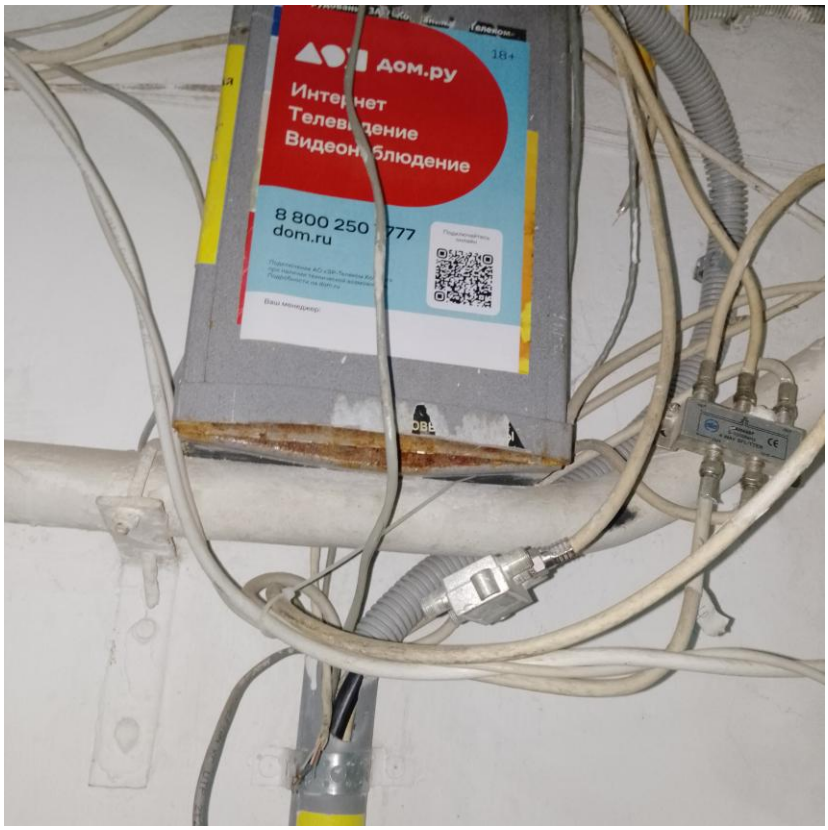


Фото 6



Продолжение Приложения 3

Фото дефектного участка

Фото 7



Фото 8



Продолжение Приложения 3

Фото дефектного участка

Фото 9



Фото 10



Продолжение Приложения 3

Фото дефектного участка

Фото 11



Фото 12



Продолжение Приложения 3

Фото дефектного участка

Фото 13



Фото 14




Продолжение Приложения 3

Фото дефектного участка

Фото 15



Фото 16

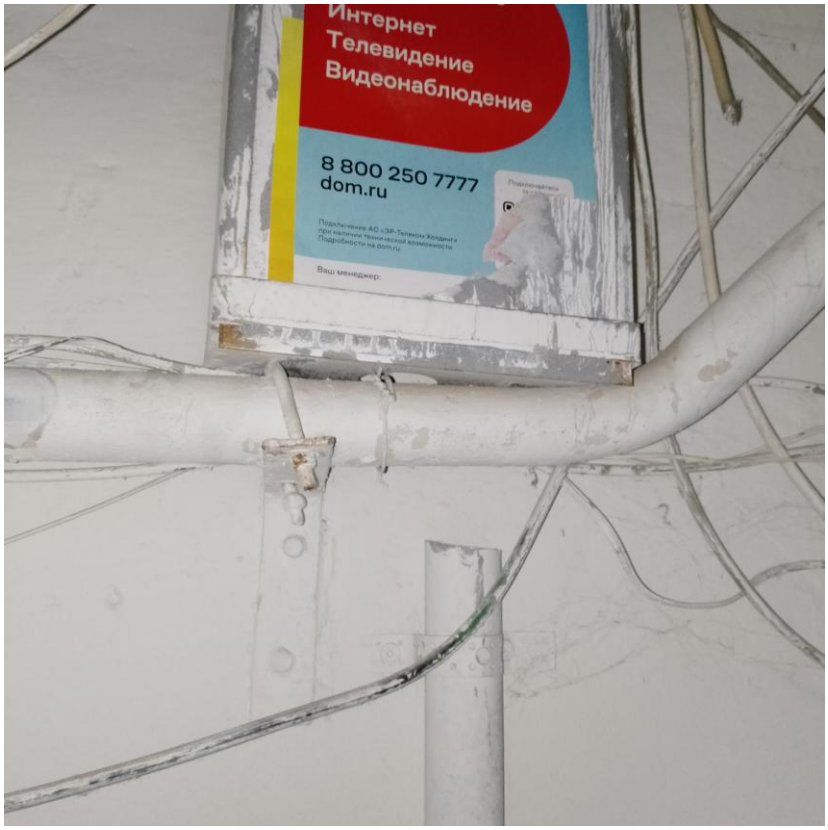

Продолжение Приложения 3

Фото дефектного участка

Фото 17



Фото 18



Продолжение Приложения 3

Фото дефектного участка

Фото 19



Фото 20



Приложение 4

Исполнитель: ООО «Профит»

Заказчик: ООО «АДС Приволжский»

ПРОТОКОЛ

по результатам ультразвуковой толщинометрии (УЗТ)

от 21.03.2025 г. № 905/2025

Внутридомовое газовое оборудование, установленное по адресу:

(наименование объекта)

Республика Татарстан, г. Казань, ул. Юлиуса Фучика, д. 105

(адрес объекта)

Контроль проводился техническими средствами: толщиномер Толщиномер ультразвуковой ТУЗ-2

Зав. № 5950 Дата поверки 13.10.2024 г.

РЕЗУЛЬТАТЫ ПРОВЕДЕНИЯ УЗТ В МЕСТАХ ОБЩЕГО ПОЛЬЗОВАНИЯ

№ участка	Условный проход, мм	Фактическая толщина, мм	№ участка	Условный проход, мм	Фактическая толщина, мм
1	32	3.2	13	32	3.1
2	32	3.1	14	25	3.1
3	32	3.1	15	32	3.1
4	25	3.0	16	32	3.2
5	25	3.1	17	32	3.2
6	32	3.2	18	25	2.9
7	32	3.1	19	25	2.9
8	32	3.2	20	32	3.2
9	25	3.0	21	25	2.9
10	32	3.1	22	32	3.1
11	25	3.1	23	25	3.1
12	25	3.1	24	25	3.0

Продолжение Приложения 4

РЕЗУЛЬТАТЫ ПРОВЕДЕНИЯ УЗТ В ЖИЛЫХ ПОМЕЩЕНИЯХ

№ квартиры	Фактическая толщина, мм			№ квартиры	Фактическая толщина, мм		
	Ду25	Ду20	Ду15		Ду25	Ду20	Ду15
1			2.5	39	3.0		2.5
2			2.5	40	2.9		2.5
3			2.6	41	3.0		2.5
4			2.5	45	3.0	2.6	2.5
6	2.9		2.5	49		2.8	2.5
8	3.0		2.5	50		2.7	2.5
10	2.9	2.6	2.5	51		2.6	2.5
11	3.0	2.7	2.6	52		2.7	2.5
12	2.9	2.7	2.5	53		2.7	2.6
18		2.7	н.д.	54		2.6	2.5
19		2.7	2.5	55		2.7	2.5
22		2.7	2.5	56		2.7	2.5
23		2.7	2.6	59		2.6	2.5
24		2.7	2.6	61		н.д.	н.д.
26		2.6	2.5	63		2.7	2.5
28		2.7	н.д.	64		2.7	2.5
29		2.7	2.5	65		2.7	2.5
30		2.7	2.5	67			2.5
31		2.6	2.5	68			2.5
34			2.5	69			н.д.
37			2.6	70			2.5

Специалист II-го уровня квалификации
Квалификационное удостоверение
№ 0039-11-28361 (УК, ВИК) от 07.07.2023 г. _____ А.А. Козлов

Подпись Ф.И.О.

Приложение 5

Исполнитель: ООО «Профит»

Заказчик: ООО «АДС Приволжский»

ПРОТОКОЛ

по результатам ультразвукового контроля (УК) сварных соединений

от 21.03.2025 г. № 905/2025

Внутридомовое газовое оборудование, установленное по адресу:

(наименование объекта)

Республика Татарстан, г. Казань, ул. Юлиуса Фучика, д. 105

(адрес объекта)

Контроль проводился
техническими средствами: дефектоскоп A1211Mini

Зав. № 4221799 Дата поверки 13.10.2024 г.

РЕЗУЛЬТАТЫ КОНТРОЛЯ

Номер сварного соединения или участка контроля	Материал, диаметр и толщина стыкуемых элементов, мм	Предельная чувствительность, мм^2	Описание обнаруженных дефектов	Оценка результатов контроля
15*	Сталь, Ø42х 3,1	1,0	Дефектов не обнаружено	Годен

*Контроледоступность сварного соединения – 80%

Специалист II-го уровня квалификации
Квалификационное удостоверение
№ 0039-11-28361 (УК, ВИК) от 07.07.2023 г. _____ А.А. Козлов

Подпись Ф.И.О.

Приложение 6

Исполнитель: ООО «Профит»

Заказчик: ООО «АДС Приволжский»

ПРОТОКОЛ

по результатам контроля влажности

от 21.03.2025 г. № 905/2025

Внутридомовое газовое оборудование, установленное по адресу:

(наименование объекта)

Республика Татарстан, г. Казань, ул. Юлиуса Фучика, д. 105

(адрес объекта)

Контроль проводился
техническими средствами: Прибор комбинированный «Testo-606-2»

Зав.№ 2080 Дата поверки 15.12.2024 г

Химические реактивы:

- 1% раствор нитрата серебра в водном растворе азотной кислоты (1:40)

- 5% раствор бихромовокислого калия

РЕЗУЛЬТАТЫ КОНТРОЛЯ

Участок контроля	*Влажность поверхностная, %	*Влажность объемная, %	Источник влаги	Расстояние до газопровода, мм	Кол-во хлорид-ионов в % к массе цемента	**Баллы
1	1.3	1.1	-	-	0,1-0,4	1-2
12	1.1	0.9	-	-	0,1-0,4	1-2
13	1.2	1.0	-	-	0,1-0,4	1-2
24	1.0	0.8	-	-	0,1-0,4	1-2

*повышенная влажность>6%;
** 0,5% - 4 балла; 0,4-0,5% - 3 балла; 0,2-0,4% - 2 балла; менее 0,2% - 1 балл.

Специалист II-го уровня квалификации
Квалификационное удостоверение
№ 0039-11-28361 (УК, ВИК) от 07.07.2023 г. _____ А.А. Козлов

Подпись Ф.И.О.

Приложение 7

Исполнитель: ООО «Профит»

Заказчик: ООО «АДС Приволжский»

ПРОТОКОЛ

по результатам контроля на наличие контакта «труба-футляр»

от 21.03.2025 г. № 905/2025

Внутридомовое газовое оборудование, установленное по адресу:

(наименование объекта)

Республика Татарстан, г. Казань, ул. Юлиуса Фучика, д. 105

(адрес объекта)

Контроль проводился
техническими средствами: Мультиметр MY-64

Зав.№ 210623284 Дата поверки 03.10.2024 г

РЕЗУЛЬТАТЫ КОНТРОЛЯ

Участок контроля	Контакт «труба-футляр»
1	Отсутствует
12	Отсутствует
13	Отсутствует
24	Отсутствует

Специалист II-го уровня квалификации
Квалификационное удостоверение
№ 0039-11-28361 (УК, ВИК) от 07.07.2023 г. _____ А.А. Козлов

Подпись Ф.И.О.

Приложение 8

Исполнитель: ООО «Профит»

Заказчик: ООО «АДС Приволжский»

ПРОТОКОЛ
визуального и измерительного контроля

от 21.03.2025 г. № 905/2025

1. В соответствии с СТО 9701105632-2021, ГОСТ 5264-80, СП 62.13330.2011, СП 42-101-2003

Внутридомовое газовое оборудование, установленное по адресу:
(наименование объекта)

Республика Татарстан, г. Казань, ул. Юлиуса Фучика, д. 105
(адрес объекта)

Контроль проводился техническими средствами:	Набор для визуального контроля	Комплект для ВИК зав.№ 2052
	Дата поверки	07.11.2024 г.

2. При контроле выявлено следующее :

2.1. На элементах газопровода коррозии не обнаружено.

Внутренний газопровод:

2.2. Подъезд №1, условный проход Ду32, 25, смотри схему контроля, фото 1, 6, 9, 10. Нарушение технологии заделки футляра (СП 42-101-2003 (п.6.7)).

2.3. Подъезд №1, условный проход Ду32, 25, смотри схему контроля, фото 3, 4, 7, 8, 10. Техническое обслуживание запорной арматуры не проведено (Постановление Правительства РФ от 14 мая 2013 г. N 410).

2.4. Подъезд №1, условный проход Ду25, смотри схему контроля, фото 4, 7. Касание газопровода со строительной конструкцией (СП 42-101-2003 (п.6.7)).

2.5. Подъезд №1, условный проход Ду32, 25, смотри схему контроля, фото 1-5, 7. Провода и кабели вблизи газопровода (СП 42-101-2003 (п.6.6); ПУЭ (п.2.1.56, п.2.1.57)).

2.6. Подъезд №1, условный проход Ду25, смотри схему контроля, фото 7. Касание газопровода со строительной конструкцией СП 42-101-2003 (п.10.216).

2.7. Подъезд №1, условный проход Ду32, 25, смотри схему контроля, фото 2, 5. Газопровод вблизи строительной конструкции СП 42-101-2003 (п.10.216).

2.8. Подъезд №2, условный проход Ду32, смотри схему контроля, фото 12, 15. Нарушение технологии заделки футляра (СП 42-101-2003 (п.6.7)).

2.9. Подъезд №2, условный проход Ду25, смотри схему контроля, фото 11, 13, 14, 17. Техническое обслуживание запорной арматуры не проведено (Постановление Правительства РФ от 14 мая 2013 г. N 410).

2.10. Подъезд №2, условный проход Ду32, 25, смотри схему контроля, фото 13, 14, 17, 18, 19. Касание газопровода со строительной конструкцией (СП 42-101-2003 (п.6.7)).

2.11. Подъезд №2, условный проход Ду32, 25, смотри схему контроля, фото 11, 14, 16, 19, 20. Провода и кабели вблизи газопровода (СП 42-101-2003 (п.6.6); ПУЭ (п.2.1.56, п.2.1.57)).

2.12. Подъезд №2, условный проход Ду32, 25, смотри схему контроля, фото 16, 17, 20. Газопровод вблизи строительной конструкции СП 42-101-2003 (п.10.216).

Продолжение Приложения 8

2.13. Несоответствия геометрических форм и размеров (овальности, переломов осей, неперпендикулярности, провисаний с образованием застойных зон) выявлено.

2.14. Состояние сварных соединений удовлетворительное. Несоответствия сварных соединений и их расположения требованиям нормативной документации выявлено.

3. Заключение по результатам визуального и измерительного контроля:

Состояние элементов газопроводов соответствует требованиям нормативно-технической документации не в полной мере.

Специалист II-го уровня квалификации
Квалификационное удостоверение
№ 0039-11-28361 (УК, ВИК) от 07.07.2023 г. _____ А.А. Козлов

Подпись Ф.И.О.

Приложение 9

Исполнитель: ООО «Профит»

Заказчик: ООО «АДС Приволжский»

ПРОТОКОЛ

по результатам контроля на герметичность

от 21.03.2025 г. № 905/2025

Внутридомовое газовое оборудование, установленное по адресу:

(наименование объекта)

Республика Татарстан, г. Казань, ул. Юлиуса Фучика, д. 105

(адрес объекта)

Контроль проводился
техническими средствами: ФП-22 (газоанализатор)

зав.№ 1405262 Дата поверки 09.09.2024 г

РЕЗУЛЬТАТЫ КОНТРОЛЯ

№ п/п	Местоположение утечки	Ф.И.О. собственника
1	-	-

Специалист II-го уровня квалификации
Квалификационное удостоверение
№ 0039-11-28361 (УК, ВИК) от 07.07.2023 г. _____ А.А. Козлов

Подпись Ф.И.О.

Слесарь по ЭРГО
Удостоверение № 826, 2025г. Э.Ф. Валиуллин

(подпись, расшифровка подписи)

Приложение 10

Исполнитель: ООО «Профит»

Заказчик: ООО «АДС Приволжский»

АКТ

по результатам пневматического испытания газопровода

от 21.03.2025 г. № 905/2025

Внутридомовое газовое оборудование, установленное по адресу:
(наименование объекта)

Республика Татарстан, г. Казань, ул. Юлиуса Фучика, д. 105
(адрес объекта)

согласно: Программы проведения технического диагностирования
(указать рабочий документ, по которому проводится контроль)

Контроль проводился техническими средствами:

Манометр КМ-22Р

Компрессор для испытания газопровода низкого давления VIRAX

Зав. № Р0005043 Дата поверки 29.10.2024 г

РЕЗУЛЬТАТЫ ИСПЫТАНИЯ

Проверка газопровода на герметичность согласно наряду-допуску № 905 от 21.03.2025 г. на производство газоопасных работ методом опрессовки давлением 500 мм вод.ст. не проводилась в связи с отсутствием технической возможности её проведения по причине отсутствия доступа во все жилые помещения при первичном обходе и по причине необслуженной запорной арматуры (Подъезд № 1-2, кран на стояк № 1-8, кран на вводе № 1).

Специалист II-го уровня квалификации
Квалификационное удостоверение
№ 0039-11-28361 (УК, ВИК) от 07.07.2023 г. _____ А.А. Козлов
Подпись Ф.И.О.

Слесарь по ЭРГО
Удостоверение № 826, 2025г. Э.Ф. Валиуллин
(подпись, расшифровка подписи)

Приложение 11

Расчёт срока возможного дальнейшего использования ВДГО № 905/2025 внутреннего газопровода, установленного по адресу: Республика Татарстан, г. Казань, ул. Юлиуса Фучика, д. 105

Задача расчета

1. Выполнить расчет срока возможного дальнейшего использования ВДГО, установленного по адресу: Республика Татарстан, г. Казань, ул. Юлиуса Фучика, д. 105, при следующих условиях:

Давление рабочее - $P_{раб}$ = 0,03 кгс/см^2

Температура рабочая - $T_{раб}$= $T_{окр. возд.}$

Расчетные параметры приняты равными максимальным значениям соответствующих рабочих параметров по данным газопровода.

2. Выполнить расчет срока возможного дальнейшего использования ВДГО, подвергающегося коррозии и изнашиванию (эрозии), по результатам данных измерения толщины стенок, проводившихся в 2025 г.

Расчет выполнен при условии соответствия элементов внутреннего газопровода, качества их сборки, механических свойств материалов и сварных соединений требованиям Руководства по безопасности «Рекомендации по устройству и безопасной эксплуатации технологических газопроводов».

Расчет:

1. Срок возможного дальнейшего использования ВДГО рассчитываем по формуле:

$$T=0,3 \times К_з \times S/V_{у.к.},$$

где Т- срок возможного дальнейшего использования ВДГО, лет;

$К_з$- коэффициент запаса;

S - толщина стенки трубы на выбранном для расчета участке газопровода, мм;

$V_{у.к.}$- условная скорость коррозии трубы, мм/год.

2. Условная скорость коррозии трубы рассчитывается по формуле:

$$V_{у.к.}=V_б \times К_{у.з.}$$

где $V_б$-базовая скорость коррозии, которая принимается 0,03 мм/год;

$К_{у.з.}$- коэффициент условий эксплуатации, который рассчитывается по следующей формуле:

$$К_{у.з.}=К_1 х К_2 х К_3 \ldots\ldots К_n$$

где $К_1, К_2, К_3 \ldots\ldots К_n$-коэффициенты.

Продолжение Приложения 11

Исходные данные для расчета:

Номер участка для расчета / Величина/значение	**№ 1**	**№ 12**	**№ 13**	**№ 24**
$К_З$ - Коэффициент запаса	0.45	0.45	0.45	0.45
Минимальная фактическая толщина стенки трубы на выбранном для расчета участке газопровода, мм;	3.2	3.1	3.1	3.0
Базовая скорость коррозии, мм/год	0.03	0.03	0.03	0.03
К1- коэффициент эксплуатации	2.0	1.5	2.0	1.5
К2- коэффициент эксплуатации	2.0	1.5	2.0	1.5
Ку.з., коэффициент условий эксплуатации	4.00	2.25	4.00	2.25
Vу.к., условная скорость коррозии, мм/год	0.12	0.07	0.12	0.07
Т, остаточный ресурс газопровода, лет	3.6	6.2	3.5	6.0

Минимальное из полученных значений срока возможного дальнейшего использования ВДГО составляет 3 года. Указанный срок не является предельным сроком эксплуатации газопровода.

Расчет произвел: _____ А.Д. Степанов

Дата 21.03.2025 г.

Приложение 12

Согласованные мероприятия по устранению неисправностей, выявленных при проведении технического диагностирования

Дефектная ведомость

Заказчик	ООО «АДС Приволжский»
Адрес	Республика Татарстан, г. Казань, ул. Юлиуса Фучика, д. 105
Объект	Внутридомовое газовое оборудование

№ п/п	Выявленная неисправность и место её расположения	Рекомендации по устранению неисправности
1	2	3
1	Внутренний газопровод	
1.1	Подъезд №1, условный проход Ду32, 25, смотри схему контроля, фото 1, 6, 9, 10. Нарушение технологии заделки футляра (СП 42-101-2003 (п.6.7)).	Пространство между газопроводом и футляром на всю его длину необходимо заделывать просмоленной паклей, резиновыми втулками или другим эластичными материалами.
1.2	Подъезд №1, условный проход Ду32, 25, смотри схему контроля, фото 3, 4, 7, 8, 10. Техническое обслуживание запорной арматуры не проведено (Постановление Правительства РФ от 14 мая 2013 г. N 410).	Провести техническое обслуживание запорной арматуры.
1.3	Подъезд №1, условный проход Ду25, смотри схему контроля, фото 4, 7. Касание газопровода со строительной конструкцией (СП 42-101-2003 (п.6.7)).	При прокладке газопроводов через конструкции зданий и сооружений газопроводы следует заключать в футляр. Края футляров должны быть на одном уровне с поверхностями пересекаемых конструкций.
1.4	Подъезд №1, условный проход Ду32, 25, смотри схему контроля, фото 1-5, 7. Провода и кабели вблизи газопровода (СП 42-101-2003 (п.6.6); ПУЭ (п.2.1.56, п.2.1.57)).	При пересечении незащищенных и защищенных проводов и кабелей с трубопроводами расстояния между ними в свету должны быть не менее 50 мм, а с трубопроводами, содержащими горючие или легковоспламеняющиеся жидкости и газы, — не менее 100 мм.
1.5	Подъезд №1, условный проход Ду25, смотри схему контроля, фото 7. Касание газопровода со строительной конструкцией СП 42-101-2003 (п.10.216).	Обеспечить расстояние между газопроводом и строительной конструкцией не менее радиуса трубы.
1.6	Подъезд №1, условный проход Ду32, 25, смотри схему контроля, фото 2, 5. Газопровод вблизи строительной конструкции СП 42-101-2003 (п.10.216).	Обеспечить расстояние между газопроводом и строительной конструкцией не менее радиуса трубы.

Продолжение Приложение 12

1.7	Подъезд №2, условный проход Ду32, смотри схему контроля, фото 12, 15. Нарушение технологии заделки футляра (СП 42-101-2003 (п.6.7)).	Пространство между газопроводом и футляром на всю его длину необходимо заделывать просмоленной паклей, резиновыми втулками или другим эластичными материалами.
1.8	Подъезд №2, условный проход Ду25, смотри схему контроля, фото 11, 13, 14, 17. Техническое обслуживание запорной арматуры не проведено (Постановление Правительства РФ от 14 мая 2013 г. N 410).	Провести техническое обслуживание запорной арматуры.
1.9	Подъезд №2, условный проход Ду32, 25, смотри схему контроля, фото 13, 14, 17, 18, 19. Касание газопровода со строительной конструкцией (СП 42-101-2003 (п.6.7)).	При прокладке газопроводов через конструкции зданий и сооружений газопроводы следует заключать в футляр. Края футляров должны быть на одном уровне с поверхностями пересекаемых конструкций.
1.10	Подъезд №2, условный проход Ду32, 25, смотри схему контроля, фото 11, 14, 16, 19, 20. Провода и кабели вблизи газопровода (СП 42-101-2003 (п.6.6); ПУЭ (п.2.1.56, п.2.1.57)).	При пересечении незащищенных и защищенных проводов и кабелей с трубопроводами расстояния между ними в свету должны быть не менее 50 мм, а с трубопроводами, содержащими горючие или легковоспламеняющиеся жидкости и газы, — не менее 100 мм.
1.11	Подъезд №2, условный проход Ду32, 25, смотри схему контроля, фото 16, 17, 20. Газопровод вблизи строительной конструкции СП 42-101-2003 (п.10.216).	Обеспечить расстояние между газопроводом и строительной конструкцией не менее радиуса трубы.

Специалист II-го уровня квалификации
Квалификационное удостоверение
№ 0039-11-28361 (УК, ВИК) от 07.07.2023 г. _____ А.А. Козлов
Подпись Ф.И.О.

Директор
ООО «АДС Приволжский» _____ А.М. Васильев
Подпись Ф.И.О.

Приложение 13

Копии удостоверений специалистов неразрушающего контроля и лиц, ответственных за проведение технического диагностирования



КВАЛИФИКАЦИОННОЕ УДОСТОВЕРЕНИЕ № 0039-11-28361

Настоящее удостоверение действительно только при наличии удостоверения о проверке знаний правил безопасности

Уровень	ПВК МЕС	ПВК ГОД	УК МЕС	УК ГОД	ВИК МЕС	ВИК ГОД	РК МЕС	РК ГОД	МК МЕС	МК ГОД
I										
II			07	2026	07	2026				
III										

ДАТА ВЫДАЧИ: 07.07.2023 г.

ООО "ЛИДЕР НК"
Независимый орган по аттестации персонала в области НК

КВАЛИФИКАЦИОННОЕ УДОСТОВЕРЕНИЕ № 0039-11-28361
ФАМИЛИЯ: КОЗЛОВ
ИМЯ: АЛЕКСАНДР
ОТЧЕСТВО: АЛЕКСАНДРОВИЧ
ГОД РОЖДЕНИЯ: 1991

УДОСТОВЕРЕНИЕ № 122-10-20-000410

Выдано «20» октября 2022 г.

Выдано Козлову Александру Александровичу
(фамилия, имя, отчество)

в том, что он 20 октября 2022 г.
(дата, месяц, год)

окончил АНО ДПО УЧЕБНЫЙ ЦЕНТР "ПРОМСТРОЙГАЗ"

по профессии: Слесарь по эксплуатации и ремонту газового оборудования

www. promstroygaz.pro

Решение квалификационной комиссии
Козлову Александру Александровичу
(фамилия, имя, отчество)

Присвоена квалификация:
Слесарь по эксплуатации и ремонту газового оборудования 5 разряд

Допускается к работам согласно должностным/производственным инструкциям
(тип машины, объекта)


www. promstroygaz.pro

Основание: Протокол квалификационной комиссии 122-10-20-0022
от «20» октября 20 22 г.

Председатель квалификационной комиссии (подпись) (ФИО)

Исполнительный директор АНО ДПО «ПромСтройГаз» П.С. Боровских
(подпись) (ФИО)

Продолжение Приложения 13

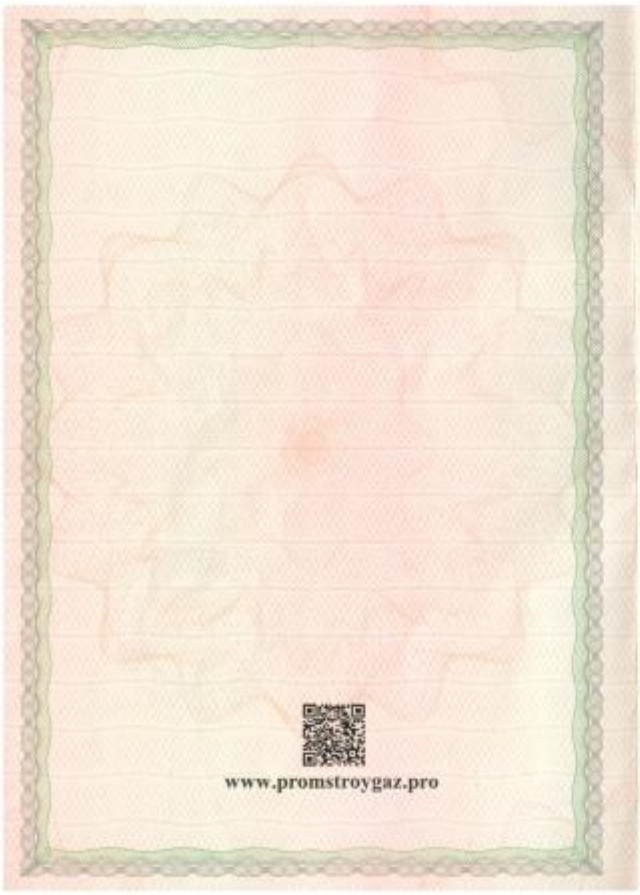

www.promstroygaz.pro



АНО ДПО
ПРОМСТРОЙГАЗ
УЧЕБНЫЙ ЦЕНТР

СВИДЕТЕЛЬСТВО
о профессии рабочего, должности служащего



АНО ДПО УЦ «ПРОМСТРОЙГАЗ»
Лицензия № 11812 от 04.03.2021 г.

Свидетельство о профессии рабочего, должности служащего является документом установленного образца

Регистрационный номер 22-10-20-00026

г. Новосибирск, 2022 г.

АНО ДПО УЦ «ПРОМСТРОЙГАЗ»
СВИДЕТЕЛЬСТВО
о профессии рабочего, должности служащего
№ С 22-10-20-00026
Настоящее свидетельство подтверждает, что
Козлов Александр Александрович
за время обучения:
с 09 сентября 2022 г. по 20 октября 2022 г.
освоил (а) основную профессиональную программу профессионального обучения по профессии:
Слесарь по эксплуатации и ремонту газового оборудования
в объеме 240 часов
Решением квалификационной комиссии
от 20 октября 2022 г.
протокол № ПО 22-10-20-00022 присвоен(а) квалификация
Слесарь по эксплуатации и ремонту газового оборудования 5 (пятого) разряда

Руководитель образовательной организации _____ /П.С. Баровских/
Председатель квалификационной комиссии _____ /П.С. Баровских/
Секретарь _____

Продолжение Приложения 13



УДОСТОВЕРЕНИЕ № 826

(личная подпись)

М.П.

Выдано «16» 05 2025 г.

Действительно при наличии отметок об аттестации и соответствующих проверках знаний (периодическая, внеочередная)

Настоящий документ удостоверяет о том, что

Валиуллин
Ильдар
Фаридович

освоил(а) образовательную программу в

АНО ДПО УТЦ «Профессионал» г. Владимир

по профессии (~~в качестве~~) слесарь по эксплуатации и ремонту газового оборудования

присвоена квалификация 5-ый разряд

2

Приложение 14

Лист учета проведения ТД
по адресу: Фучика 105
подъезд: 2 дата «11» 03 2025 г.

№ кв	ФИО	Подпись
30	Журавлева Ф.Ф.	
29	Мейбоб О.Э.	
28	Ромашова З.П.	
22	Сафина З.И.	
23	Исламов Д.А.	
24	Нуриев С.В.	
18	Хисматова З.Х.	
19	Ананьева И.А.	
12	Гаранкова Г.М.	
17	Исмагилов Р.И.	
8	Савельева В.Р.	

Руководитель работ Чехлов С.А.
Подпись

Лист учета проведения ТД
по адресу: Фучика 105
подъезд: 2 дата «11» 03 2025 г.

№ кв	ФИО	Подпись
68	Нуриева Р.И.	
67	Калимуллин И.Р.	
69	Исхакова Р.Р.	
63	Набиева З.И.	
59	Волкова И.С.	
56	Рахимова А.	
51	Шагаева А.Ш.	
54	Афанасьева С.В.	
45	Шарзиахметова Р.	
37	Иванова А.З.	
4	Рахимова З.И.	
2	Зиганшина Р.Р.	
1	Вахобова Ф.А.	

Руководитель работ Чехлов С.А.
Подпись

Приложение 15

АКТ
отсутствия доступа (допуска) сотрудников ООО «ПРОФИТ» в жилые помещения многоквартирного дома при проведении работ по техническому диагностированию внутридомового газового оборудования

г.Казань «11» 03 2025 г.

Мы, ниже подписавшиеся, составили настоящий Акт о том, что при первичном (повторном) выезде для проведения работ по техническому диагностированию внутридомового газового оборудования по адресу ул. Юлиуса Фучика 105, находящемуся в управлении УК ЖЭС Приволжского р-на в рамках исполнения договора №_____ от «_____» _____ 20___г., во время, указанное в графике проведения работ, прилагаемое к договору, не обеспечен доступ (допуск) представителей ООО «ПРОФИТ» в нижеперечисленные жилые помещения (квартиры).

Время проведения работ донесено до Заказчика заблаговременно при подписании договора и утверждении графика проведения работ Заказчиком.

Доступ (допуск) не обеспечен в следующие жилые помещения в указанное время:

Кол-во квартир в доме	Номера квартир, в которые не предоставлен доступ (допуск)
68/24	3,5,6,7,9,10,13,14,15,16,17,20,21,25,26,27,31, 32,33,34,35,36,39,40,41,42,43,44,46,47,48, 49,50,52,53,55,57,58,60,61,62,64,65,66,70. кв. 38 - без газа

Собственник (представитель собственника) жилого помещения № 68 _____ подпись Нурдинова Р.Ш. ФИО

Собственник (представитель собственника) жилого помещения № 67 _____ подпись Калимуллин И.Р. ФИО

Приложение 16

Лист учета проведения ТД
по адресу: Фучика 105
подъезд: 3 дата «21» 03 2025 г.

№ кв	ФИО	Подпись
34	Шамсутдинов А.Р	
31	Хусаинов М.И	
26	Юсупова М.О	
10	Хисамиев К.В.	
6	Соколовский Г.Р	
3	Салимов М.В.	
34	Озерова О.В	
40	Булатов А.И.	
41	Сергеичева Е.Н	

Приложение 17

АКТ

отсутствия доступа (допуска) сотрудников
ООО «ПРОФИТ» в жилые помещения многоквартирного дома
при проведении работ по техническому
диагностированию внутридомового газового
оборудования

г.Казань «21» 03 2025

Мы, ниже подписавшиеся, составили настоящий Акт о том, что при первичном (повторном) выезде для проведения работ по техническому диагностированию внутридомового газового оборудования по адресу Юлиуса Фучика 105, находящемуся в управлении УК АЦС Тоншаевского р-на в рамках исполнения договора №_____ от «_____» _____ 20___г., во время, указанное в графике проведения работ, прилагаемое к договору, не обеспечен доступ (допуск) представителей ООО «ПРОФИТ» в нижеперечисленные жилые помещения (квартиры).

Время проведения работ донесено до Заказчика заблаговременно при подписании договора и утверждении графика проведения работ Заказчиком.

Доступ (допуск) не обеспечен в следующие жилые помещения в указанное время:

Кол-во квартир в доме	Номера квартир, в которые не предоставлен доступ (допуск)
69/42	5, 7, 8, 13, 14, 15, 16, 17, 20, 21, 25, 27, 32, 33, 35, 36, 41, 43, 44, 46, 47, 48, 57, 58, 60, 62, 66.

Собственник (представитель собственника) жилого помещения № 39 _____ подпись Шигапов ХФ ФИО

Собственник (представитель собственника) жилого помещения № 57 _____ подпись Нуреева НЧ ФИО

Приложение 18

Перечень
нормативно-технической документации,
использованной при проведении технического диагностирования

1. О промышленной безопасности опасных производственных объектов. Федеральный закон от 21.07.1997 г. № 116-ФЗ (с изменениями).
2. О мерах по обеспечению безопасности при использовании и содержании внутридомового и внутриквартирного газового оборудования. Постановление Правительства РФ от 14.05.2013 г. № 410 (с изменениями и дополнениями).
3. О порядке поставки газа для обеспечения коммунально-бытовых нужд граждан. Постановление Правительства РФ от 21 июля 2008 года № 549 (с изменениями и дополнениями).
4. Об утверждении Порядка содержания и ремонта внутридомового газового оборудования в Российской Федерации. Приказ Министерства регионального развития Российской Федерации от 26 июня 2009 года № 239 зарегистрирован в Минюсте РФ 17 сентября 2009 года, регистрационный № 14788.
5. Об утверждении методических рекомендаций по контролю за техническим обслуживанием и состоянием внутридомового газового оборудования. Приказ Министерства природных ресурсов и экологии Российской Федерации, Федеральной службы по экологическому, технологическому и атомному надзору от 2 декабря 2009 года № 1001. (с изменениями).
6. Положение о диагностировании технического состояния внутренних и газопроводов жилых и общественных зданий. Общие требования. Методы диагностирования, утверждены Приказом Госстроя России № 101 от 3 мая 2000 года (МДС 42-1.2000).
7. ГОСТ 20415-82 Контроль неразрушающий. Методы акустические. Общие положения.
8. ГОСТ 16037-80* Соединения сварные стальных трубопроводов. Основные типы, конструктивные элементы и размеры.
9. ГОСТ 22690-2015 Бетоны. Определение прочности механическими методами неразрушающего контроля.
10. ГОСТ 17624-2012 Бетоны. Ультразвуковой метод определения прочности.
11. ГОСТ Р ИСО 24497-3-2009 Контроль неразрушающий. Метод магнитной памяти металла. Часть 2. Контроль сварных соединений.
12. ГОСТ Р 55614-2013 Контроль неразрушающий. Толщиномеры ультразвуковые. Общие технические требования.
13. ГОСТ Р ИСО 24497-2-2009 Контроль неразрушающий. Магнитная память металла. Часть 2. Общие требования.
14. ГОСТ Р 55724-2013 Контроль неразрушающий. Сварные соединения. Методы ультразвуковые.
15. ГОСТ 30494-2011 Здания жилые и общественные. Параметры микроклимата в помещениях.
16. ГОСТ 26433.1-89 Система обеспечения точности геометрических параметров в строительстве. Правила выполнения измерений. Элементы заводского изготовления.
17. ГОСТ 30494-2011 Здания жилые и общественные. Параметры микроклимата в помещениях.

Продолжение Приложения 18

18. СНиП II-13.10-58 «Жилые здания. Нормы проектирования».
19. СНиП II-Л.1-71 «Жилые здания. Нормы проектирования».
20. СНиП 2.08.01-85 «Жилые здания. Нормы проектирования».
21. СНиП 2.08.01-89 «Жилые здания. Нормы проектирования».
22. СНиП 31-01-2003 «Здания жилые многоквартирные. Нормы проектирования».
23. СП 42-101-2003 Общие положения по проектированию и строительству газораспределительных систем из металлических и полиэтиленовых труб.
24. СП 42-102-2004 Проектирование и строительство газопроводов из металлических труб.
25. СП 54.13330.2011 Свод правил. Здания жилые многоквартирные.
26. СП 62.13330.2011 Свод правил. Газораспределительные системы.
27. СП 33.13330.2012 Свод правил. Расчет на прочность стальных трубопроводов.
28. СП 28.13330.2012 Свод правил. Защита строительных конструкций от коррозии.
29. СП 60.13330.2012 Отопление, вентиляция и кондиционирование воздуха. Актуализированная редакция СНиП 41-01-2003.
30. СП 402.1325800.2018 Здания жилые. Правила проектирования систем газопотребления.
31. СТО 9701105632-003-2021 Инструкция по визуальному и измерительному контролю.
32. СТО РНТСО 004-03 Контроль неразрушающий. Сварные соединения оборудования и конструкций. Метод магнитной памяти металла (ММП-контроль).
33. Инструкция по безопасному использованию газа при удовлетворении коммунально-бытовых нужд (утверждена приказом Министерства строительства и жилищно-коммунального хозяйства Российской Федерации от 5.12.2017 г. № 1614/пр)
34. ГОСТ Р 58095.4-2021 Системы газораспределительные. Требования к сетям газопотребления. Часть 4.
35. ГОСТ Р 54983-2012 Системы газораспределительные. Сети газораспределения природного газа.
36. ПБ 03-440-02 Правила аттестации персонала в области неразрушающего контроля, утверждены Постановлением Госгортехнадзора России от 23.01.2002 г № 3.
37. ВСН 58-88 (Р) Положение об организации и проведении реконструкции, ремонта и технического обслуживания зданий, объектов коммунального и социально-культурного назначения.
38. Методика по комплексному техническому диагностированию внутренних газопроводов ООО «ПОЛИТЕСТ-Инжиниринг» НП «СЭЦ промышленной безопасности».